Double-height media wall


FF hall · 2221 × 6556 mm



2221 × 6556	55"	4 × 11
wall	TV	squares


Front elevation

1:30

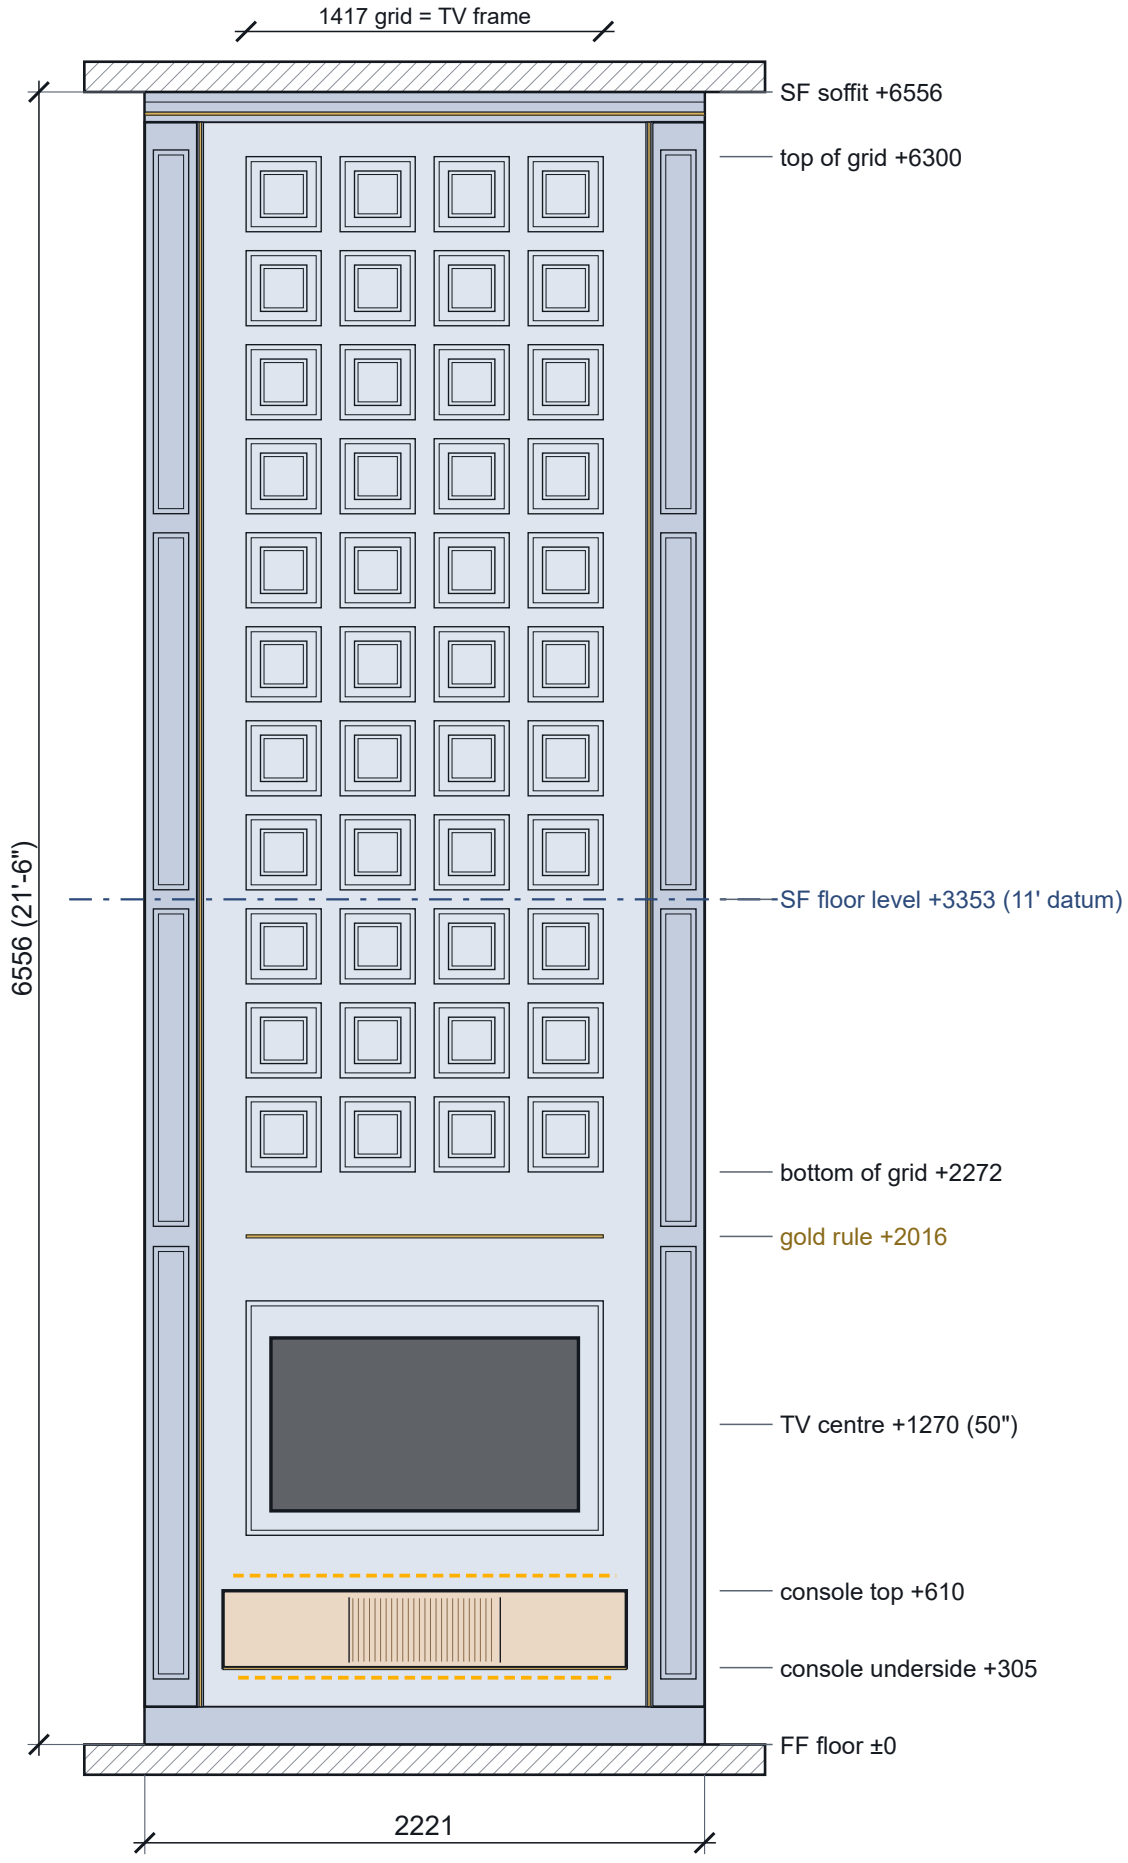


TV & console zone


1:13

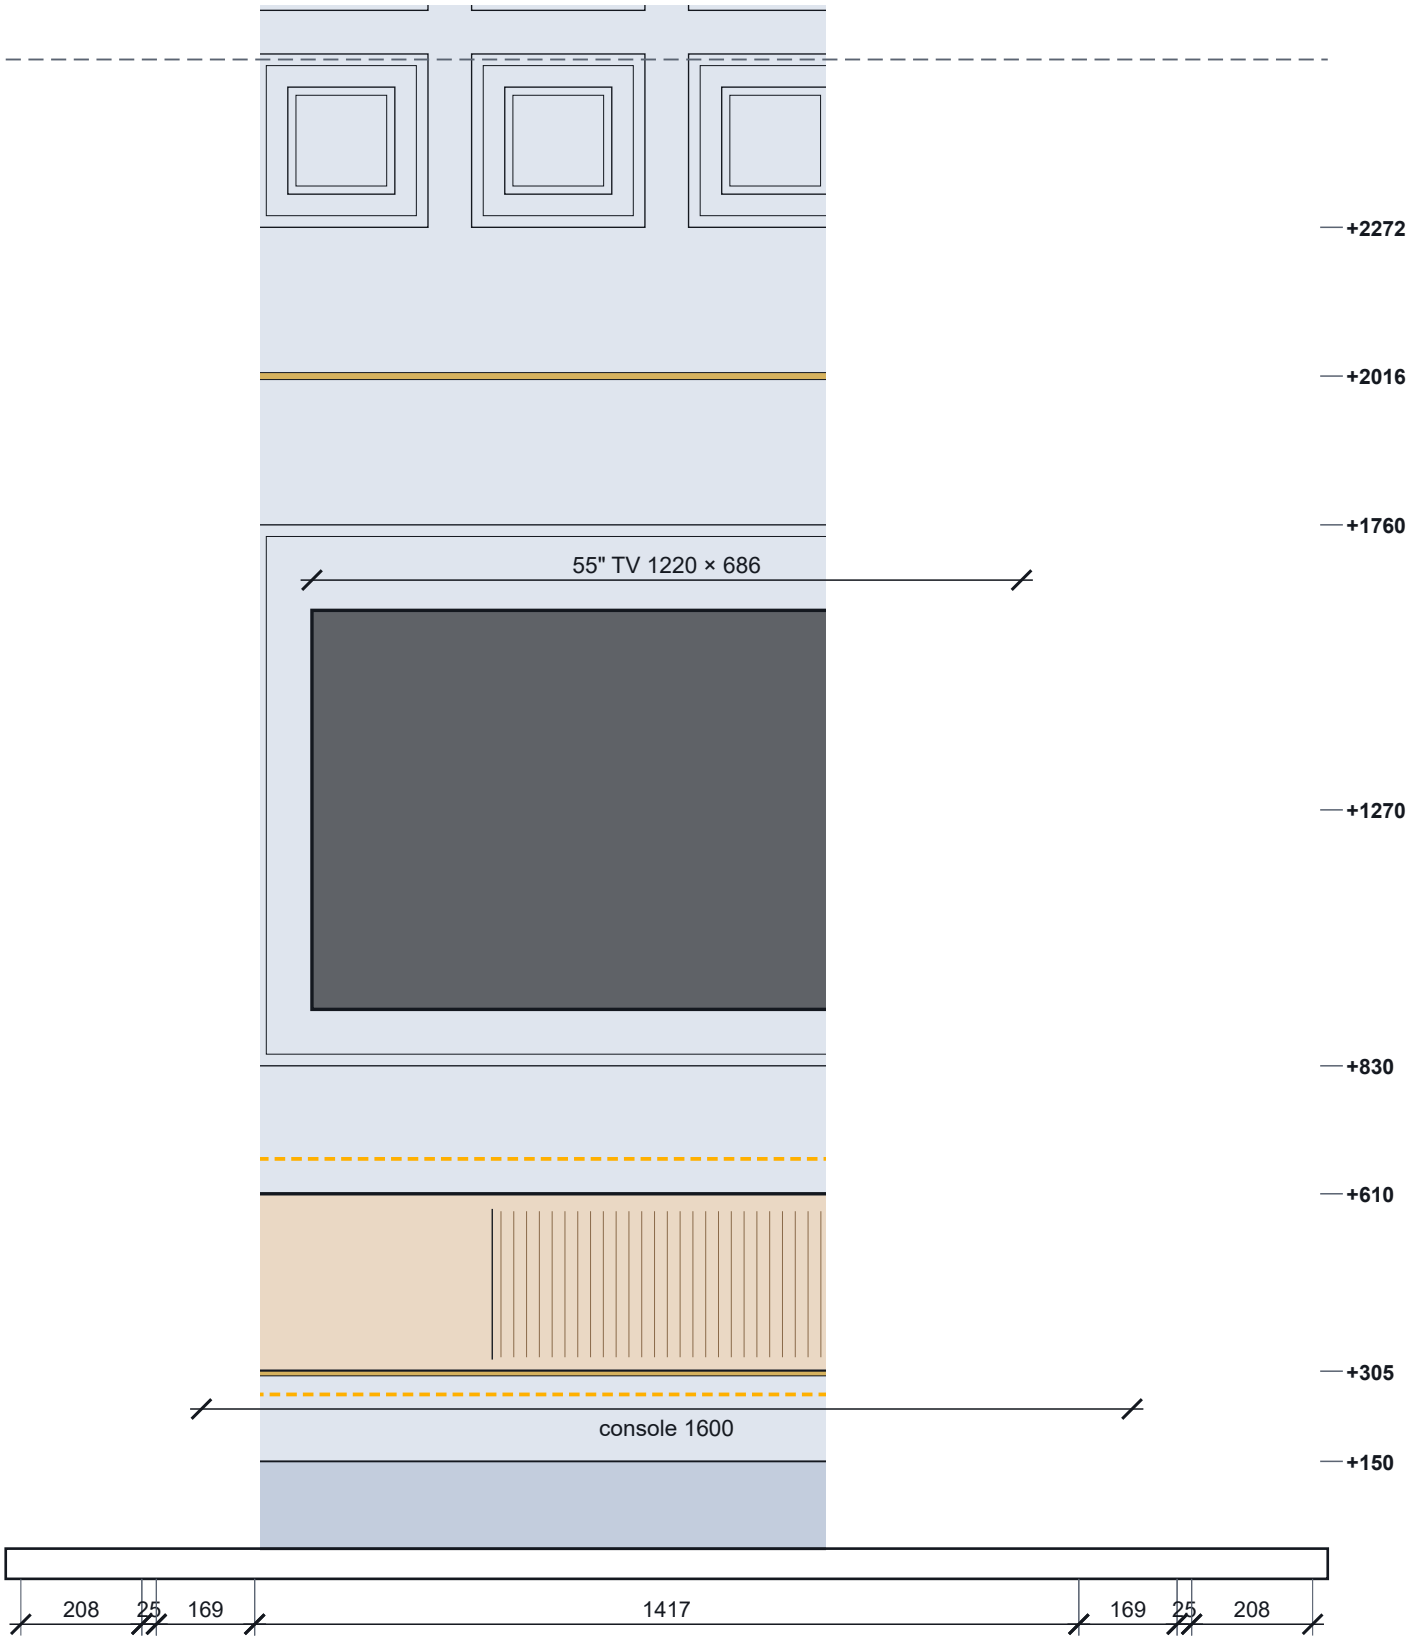


Squares & mouldings

module 1:3.5 · profiles 3:1

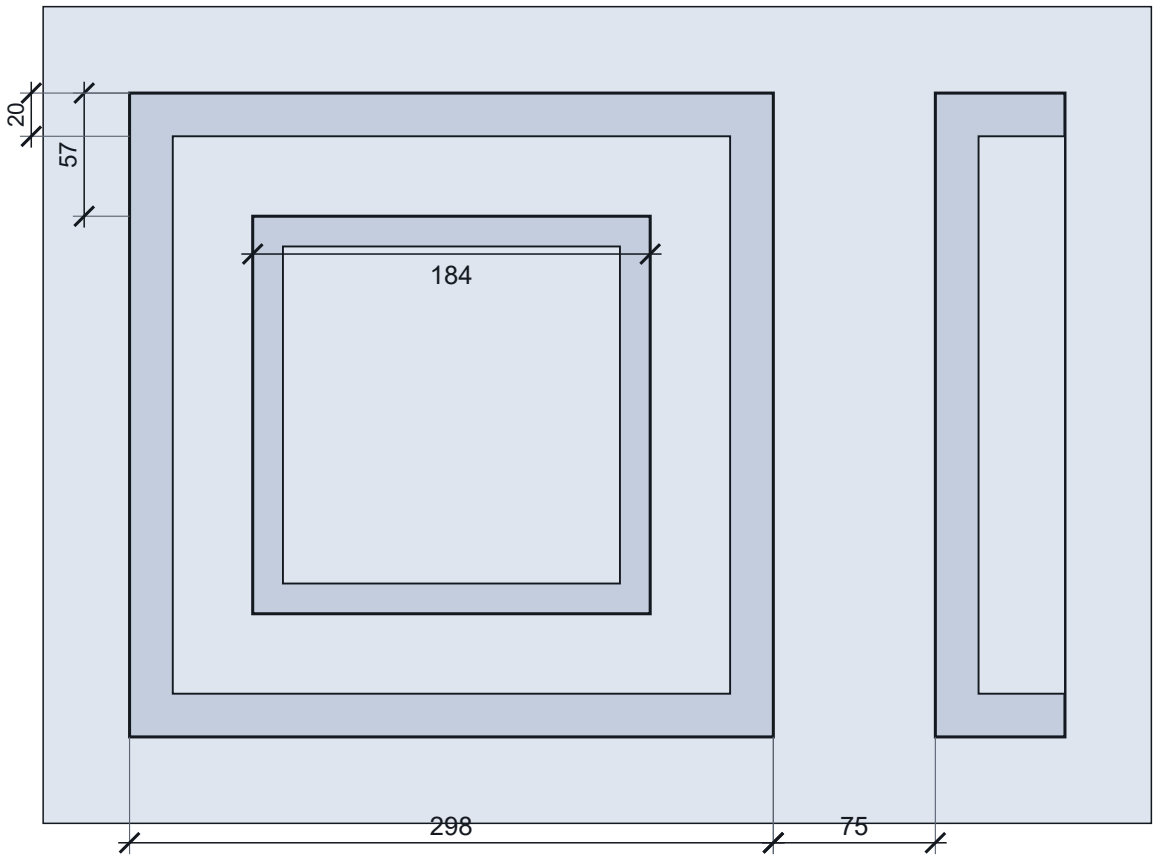

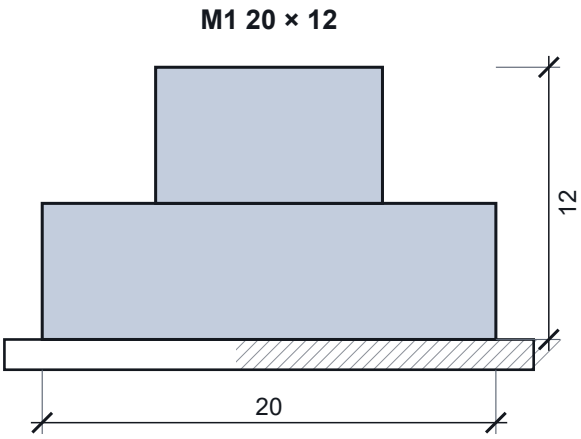


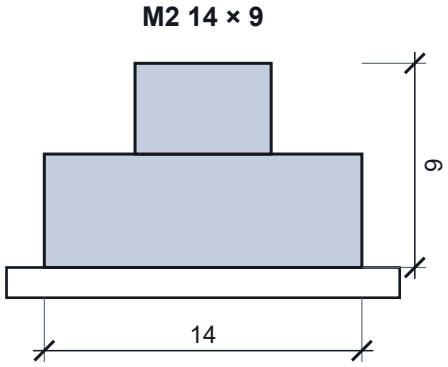

M1 PU 20 × 12 — outer squares, TV frame, pilaster panels
M2 PU 14 × 9 — inner squares


Section A–A

1:30

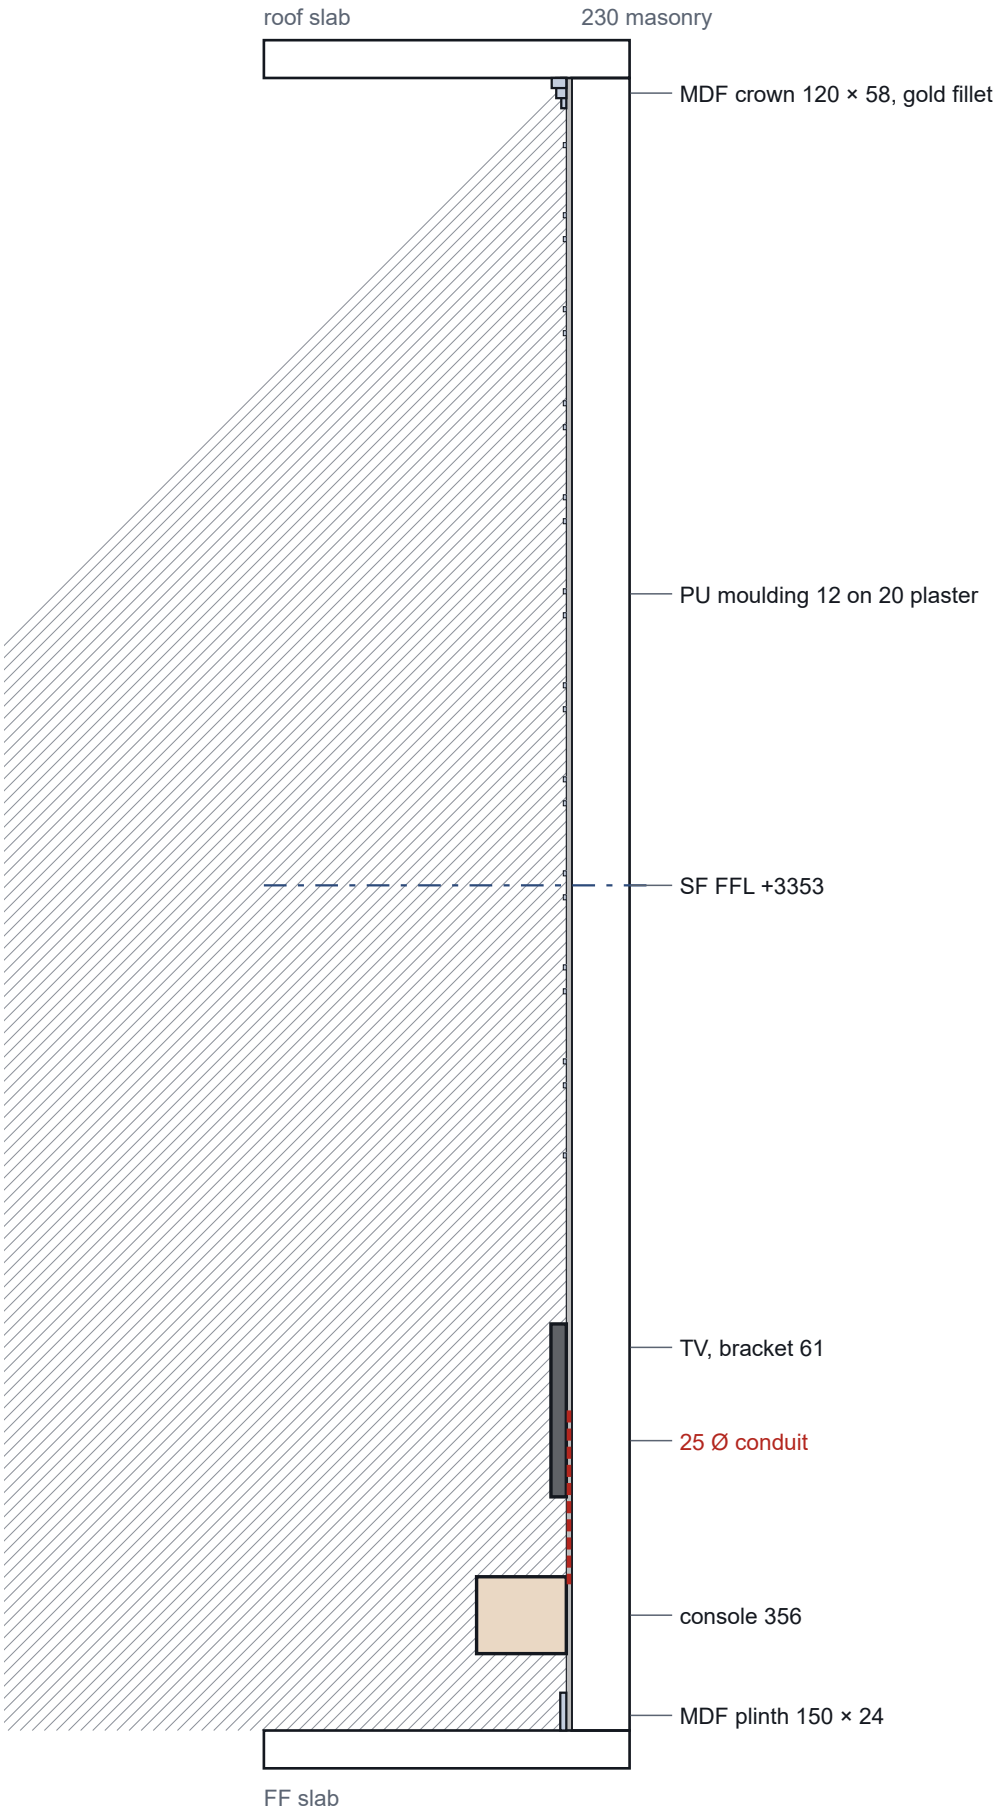

Plan B–B + gold reveal

plan at +1200, 1:12 · reveal 2:1

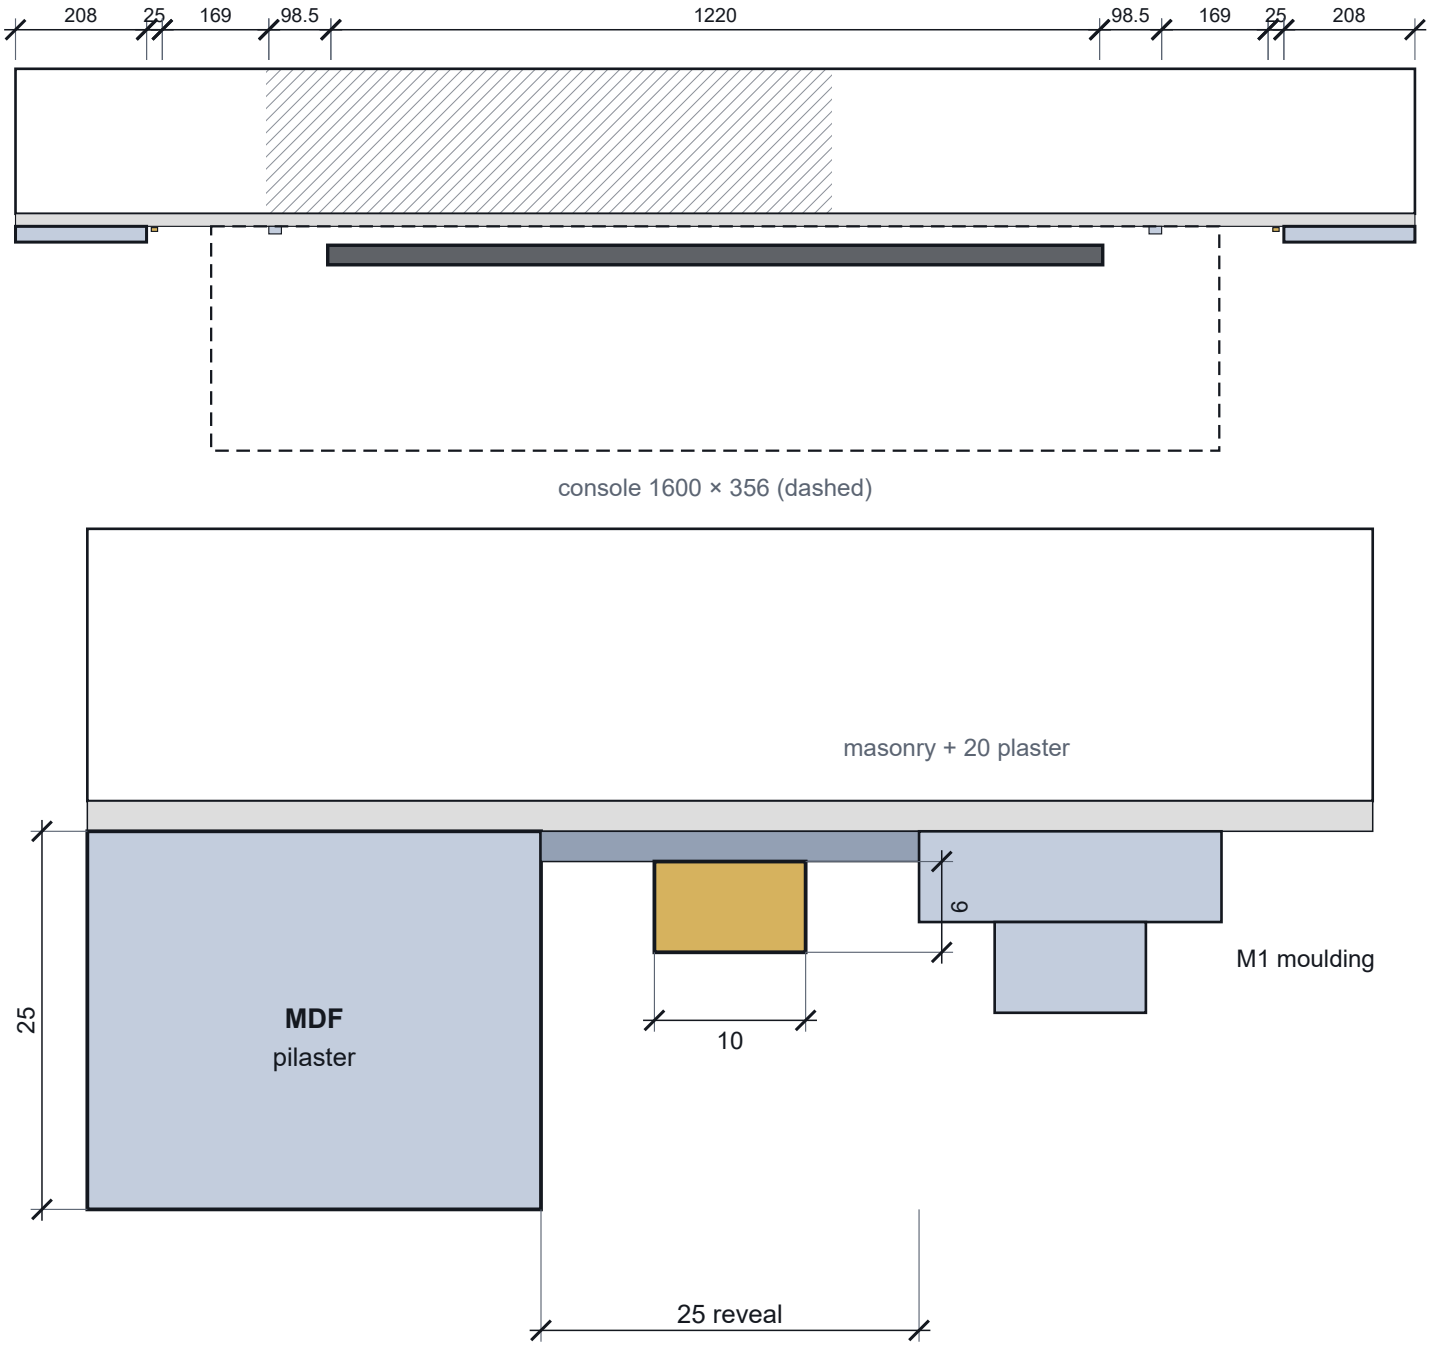


Gold-anodised aluminium flat bar 10 × 6, continuous plinth → crown, 2 × 6.29 m


Console, LED, crown

console 1:6 · crown 1:3

Console section 1:6

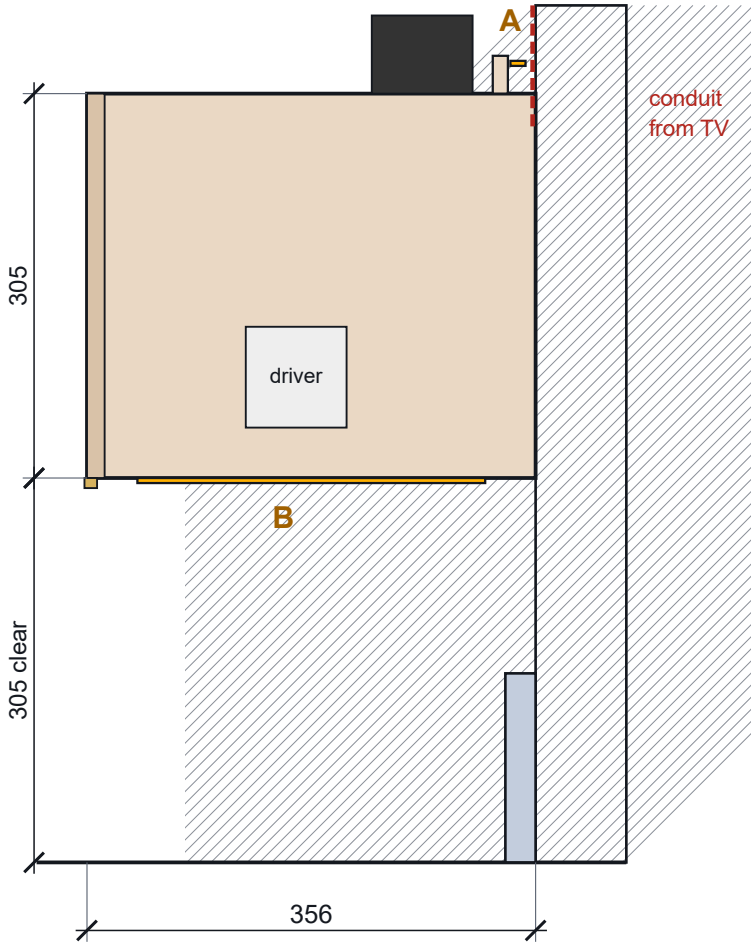

Crown 1:3

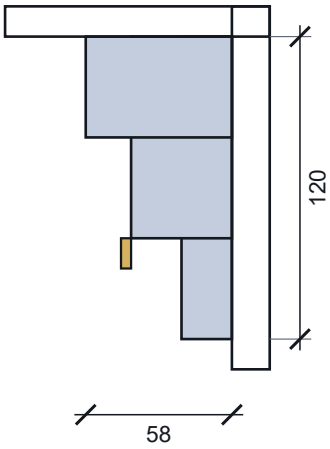

A	LED up-wash behind 30 mm upstand
B	LED under-glow, 40 set back
LED	24 V COB · 2700–3000 K · CRI ≥ 90 · ~3 m · 60 W driver · dimmable
Console	walnut veneer on 18 ply · 1600 × 305 × 356 · steel French cleat

Specification

Wall	plaster + putty · matte emulsion, deep navy #22385B
Squares	44 (4 × 11) · 298 outer M1 + 184 inner M2 · 75 gap · grid 1417
Pilasters	MDF 208 × 25 · PU satin navy #1A2C48 · M1 panels 140 wide
Gold	gold-anodised Al · 10 × 6 bar 2 × 6.29 m · rule 1417 × 12 @ +2016 · crown fillet 12
Mouldings	PU · M1 20 × 12 · M2 14 × 9 · painted with the wall, satin
Crown	MDF stepped 120 × 58
Plinth	MDF 150 × 24 · blocks 31 under pilasters
TV	55" (1220 × 686) · centre +1270 · fixed bracket · M1 frame 1417 × 930
Power	25 Ø conduit TV → console · 2 sockets behind TV · 2 sockets + LAN in console
Console	walnut veneer · 1600 × 305 × 356 · underside +305 · 500 | 600 fluted | 500
LED	console only · up-wash + under-glow · 24 V COB 2700–3000 K · ~3 m
Pendants	linen drum cluster · +3600 … +4400

Finishes

painted field

MDF / mouldings

gold aluminium

walnut

TV

LED (console)

Evening



Day





Details

